
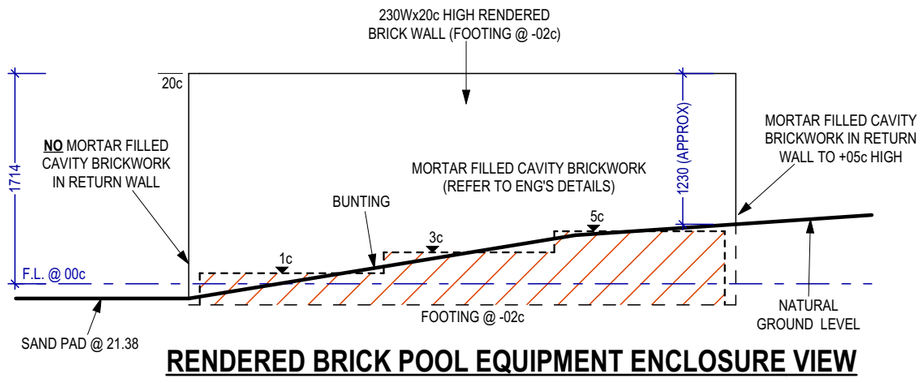


RENDERED BRICK POOL EQUIPMENT ENCLOSURE VIEW

SCALE 1:50

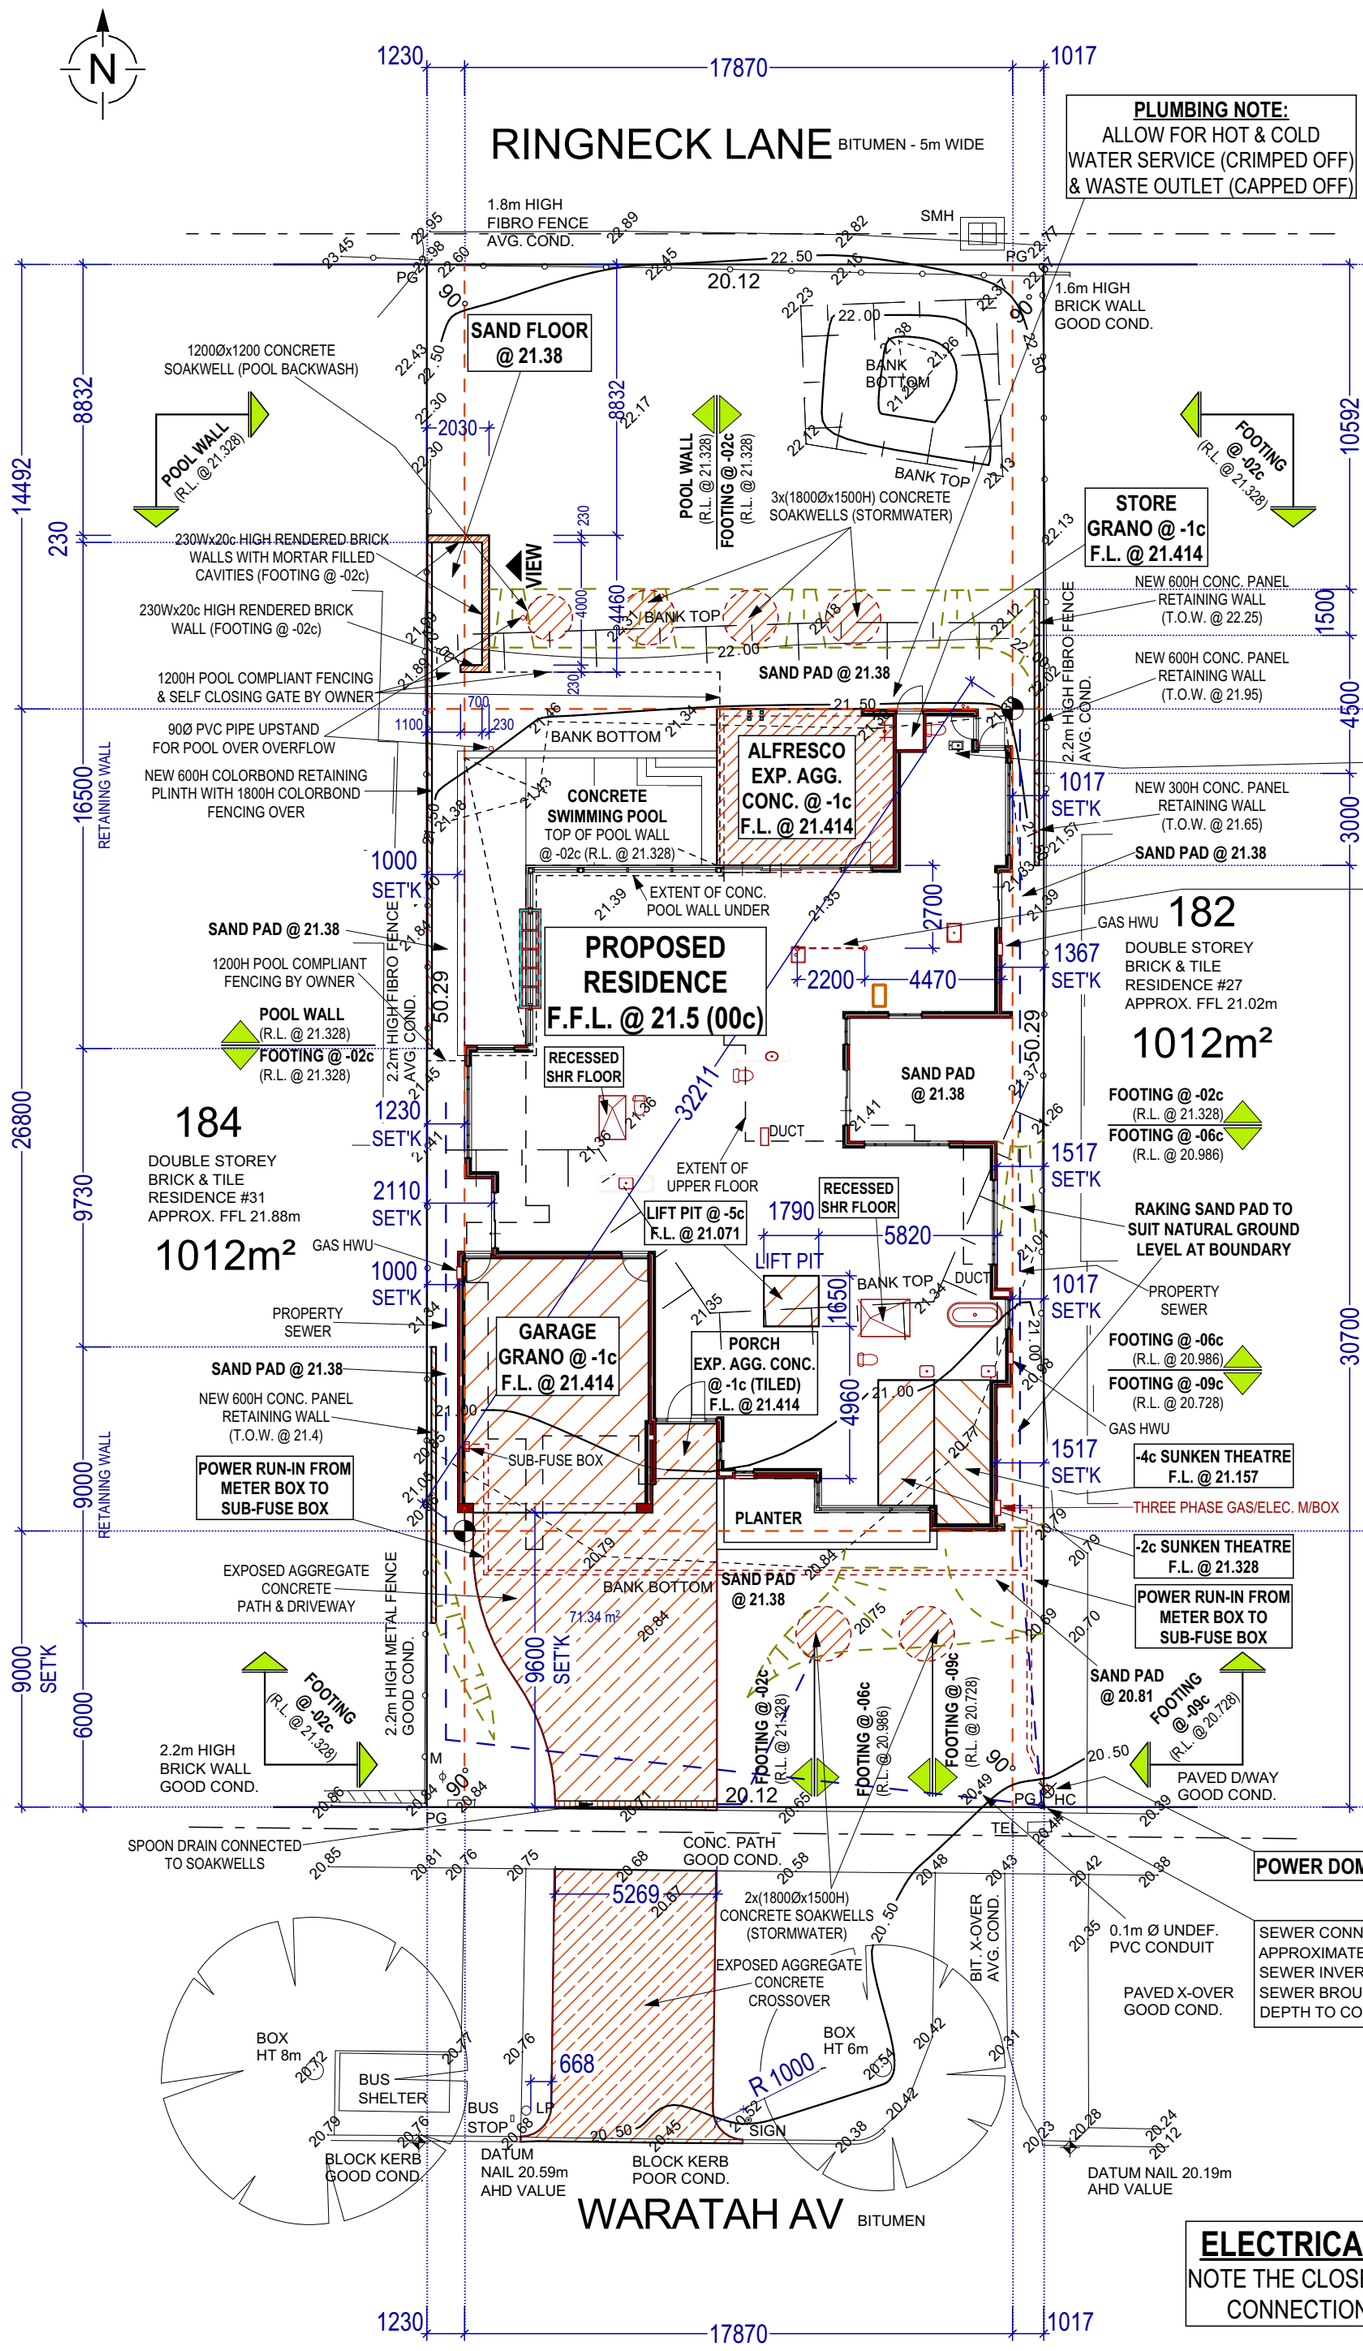

PLUMBING NOTE:
ALLOW FOR HOT & COLD WATER SERVICE (CRIMPED OFF) & WASTE OUTLET (CAPPED OFF)

NOTE:
LOCATION OF POOL BALUSTRADE & SELF CLOSING GATE TO BE CONFIRMED BY OWNER

PLUMBING NOTE:
ALLOW FOR WALL BASIN TO POWDER ROOM 2 WITH WASTE OUTLET CHASED INTO BRICKWORK

PLUMBING NOTE:
ALLOW FOR CONDUIT UNDER SLAB FOR POWER RUN TO KITCHEN ISLAND CUPBOARD

ELECTRICAL / PLUMBING NOTE:
NOTE THE CLOSE PROXIMITY OF THE SEWER CONNECTION AND THE POWER DOME

SERVICE LEGEND

POWER
- CONSUMER POLE ○ CP
- POWER POLE ○ PP
- LIGHT POLE ○ LP
- STAY POLE ○ SP
- S. WIRE ANCHOR ○ SWA
- UNI PILLAR ⊗
- EXPOSED CABLES ○ EC

GAS
- PRE-LAID CONN. ○ GPL
- METER □ GM

SEWERAGE
- MANHOLE ◯ SMH
- INSPECT. SHAFT ○ IS
- INSPECT. OPENING ○ IO
- HOUSE CONNECTION ○ HC
- HOUSE CONN. INDICATOR ○ HCI
- INSPECT. SHAFT CONNECTION ○ ISC

TELE.
- PIT ▭ TEL
- PRE-LAID CONN. ○ TPL

DRAINAGE
- MANHOLE ◯ DMH
- GULLY PIT
- LOT PIT ◯ LDP
- HOUSE CONN. ○ DHC
- SIDE ENTRY PIT
- COMBINATION ENTRY PIT

WATER
- STOP VALVE ○ WSV
- HYDRANT ○ HY
- FLUSH POINT ○ FP
- WATER TAP ○ WTP
- WATER METER ○ M
- PRE-LAID CONN. ○ WPL

SURVEY
- DATUM NAIL ✦
- PEG FOUND ○ PF
- PEG DISTURBED ○ PD
- PEG GONE PG
- STAKE FOUND ○ STF

LOT RECORDS

STATUS / LOT SERVICE	LOCATED	AVAILABLE	NO SERVICE	CONFIRM
WATER	✓			
SEWERAGE	✓			
GAS		✓		✓
TELE.	✓			
DRAINAGE				✓
POWER U/G	✓			
O/H			✓	

AREA: ESTAB 03/1920

COASTAL DISTANCE 1.5-10km

LOT: 183
AREA: 1011 m²

SERVICES MARKED CONFIRM REQUIRE BUILDER / CLIENT TO CONFIRM POSITION & / OR AVAILABILITY ON SITE. AHD CONNECTION OBSERVED FROM LANDGATE'S GEODETIC RECORDS.

GROUND COVER

SANDY

TITLE	: FEATURE SURVEY
CLIENT	: RADHAKRISHNAN & KOLOTH
BUILDER	: ATRIUM HOMES (WA) PTY LTD

LINKS SURVEYING
P: (08) 9354 8511
W: www.linkssurveying.com.au
E: info@linkssurveying.com.au

LOT	: 183 No. 29 WARATAH AV		
SUBURB	: DALKEITH	DP : 202213	
AUTHORITY	: CITY OF NEDLANDS	C/T : 1071/153	
UBD REF	: 287 E 15	GPS : S 31.99444°	E 115.80586°

5 0 2.5 5 10 15

SHEET	BUILDER'S REF	SURVEYED	SCALE @ A2	DWG No	REV
1 of 1	2305	16/02/23	1:200	46679-01-100	A

NOTE This PLAN is current at the Surveyed Date, NOT FOR CONSTRUCTION purposes without site corroboration. The cadastral boundary POSITION is APPROXIMATE & requires survey confirmation - Check Landgate Plan & Certificate of Title for Encumbrances including Easements, Caveats, Covenants etc. All SERVICES require verification from the relevant AUTHORITY - suggest contacting "Dial Before You Dig" for underground services & a site inspection. © STANDFAST NOMINEES 1996

ATRIUM HOMES
9 WILLCOCK STREET,
ARDROSS WA 6153,
PH: 6310 8888 FAX: 6310 8889
© COPYRIGHT ATRIUM HOMES

PROPOSED RESIDENCE

FOR:- **RADHAKRISHNAN & KOLOTH**
LOT N°: **183 (#29) WARATAH AVENUE, DALKEITH**

*NOTE: * ALL PLANS & ELEVATIONS ARE DIAGRAMATIC ONLY AND SHOULD NOT BE USED TO SCALE EXACT SIZES. BRICK MEASUREMENTS DO NOT ALLOW FOR PLASTERING FINISH.*
** THE COPYRIGHT OF THIS HOUSE DESIGN IS THE SOLE PROPERTY OF ATRIUM HOMES (WA) Pty Ltd AND THERE IS NO IMPLIED LICENCE FOR ITS USE.*

VO 3 PVN 8/9/23
VO 12 & 13 PVN 14/12/23
VO 14-17 PVN 7/2/24
VO 19 PVN 26/2/24
VO 21 PVN 6/9/24

SHEET 1 OF 14

JOB NUMBER: ***2305***

DRAWN	DATE	CHANGES
PVN	02/03/2023	PVN 15/8/23